

KEY PLAN

NOTES:

1. ALL DIMENSIONS AND ELEVATIONS AND CO-ORDINATES ARE IN MM.
2. LOCATION OF JUNCTION BOXES, INSTRUMENTS ARE INDICATIVE ONLY. POSITION MAY BE CHANGED AT SITE FROM THE POINT OF VIEW OF MAINTENANCE, EASE OF OPERATION OR TO AVOID OBSTRUCTIONS etc.
3. FOR ACTUAL LOCATION OF INSTRUMENT IMPULSE TAPPING POINTS REFER TO PIPING GENERAL ARRANGEMENT DRAWING AND PIPING ISOMETRICS OR VESSEL DRAWINGS.
4. THE INSTRUMENT SHALL BE LOCATED WITH SUFFICIENT CLEARANCE FOR INSTALLATION, MAINTENANCE AND REPLACEMENT, THEY SHALL BE ACCESSIBLE FROM GROUND OR PLATFORM OR WALKWAY.
5. INSTRUMENT SHALL BE MOUNTED GENERALLY BETWEEN 1.30 METERS TO 1.50 METERS ABOVE GRADE / PLATFORM.
6. WHEREVER INSERT PLATE NOT AVAILABLE, SAME SHALL BE PROVIDED BY INSTRUMENT CONTRACTOR WITH ANCHOR FASTENER.
7. ACTUAL LOCATION & ELEVATIONS OF INSTRUMENTS SUPPLIED BY PACKAGE VENDOR TO BE DETERMINED AT SITE.
8. ALL INSTRUMENTS NOT INDICATED IN THESE LOCATION PLAN ARE IN A DIFFERENT AREA OR IN THE EXISTING AREAS.


LEGEND:

- ● : SENSING ELEMENT REQUIRING WIRING/TUBING TO TRANSMITTER.
- ▲ : DISCRETE DEVICE
- ■ : ANALOG DEVICE 4-20mA 2 WIRE
- ◣ : ANALOG DEVICE WITH POWER SUPPLY 4 WIRE
- : PAN,TILT & ZOOM CCTV CAMERA
- : JUNCTION BOX
- : INST. LOCAL CONTROL PANEL
- : CONTROL VALVE
- : SOLENOID VALVE
- : ON/OFF VALVE
- : MOTORIZED OPERATED VALVE
- : SLIDING GATE VALVE
- : INSTRUMENT AIR MANIFOLD
- XXXX / XXX / XXX — INST. TAG No. / XXXX-XXX-XXX — JUNCTION BOX No. / IA — INST. AIR SUPPLY FROM MAIN HEADER / EL. XXX.XXX — INSTRUMENT ELEVATION
- XXXX-JBX-XXX — JBA – ANALOG JB, JBD – DIGITAL JB, JBP – POWER JB — JUNCTION BOX No. / EL. XXX.XXX — JUNCTION BOX ELEVATION
- B.O.T : BOTTOM OF TRAY
- T.O.S : TOP OF STRUCTURE
- PLT. : PLATFORM

HOLD LIST:

XXXXXXXXXXXXX	XXXXXXXXXXXXXXL	XXXXXXXXXX
DRAWING NO.	TITLE	REMARKS

REFERENCE DRAWINGS

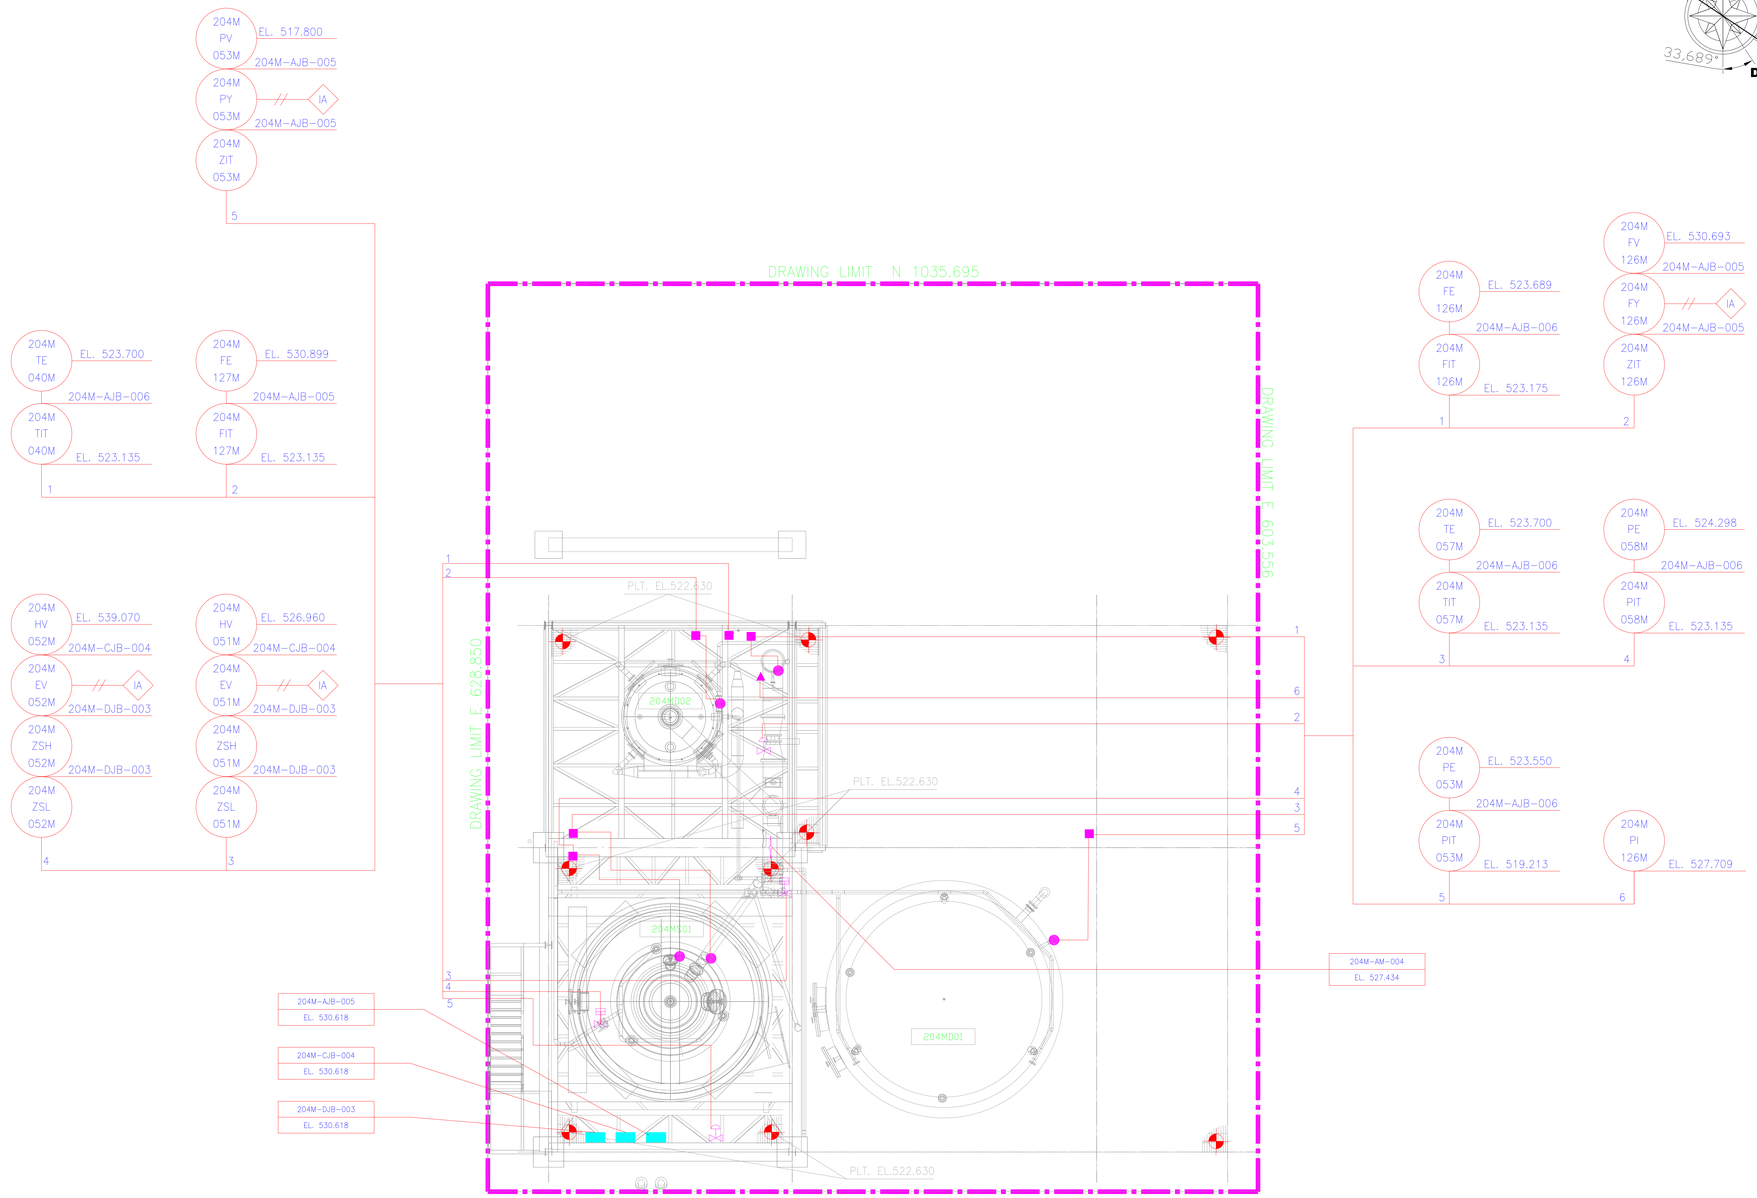

PLAN FROM EL. 521.860 AND ABOVE

SCALE 1:100

LOOKING PLAN

This drawing was generated using AutoCAD and must not be altered manually. Do not Scale.

This drawing is the property of JESA. Neither this document nor any information herein shall be copied or reproduced in any manner, loaned or otherwise disposed of, or used for any purpose whatsoever without the prior written permission of JESA. If this document is loaned by or with the authority of JESA, the borrower in consideration of such loan, agrees to the foregoing conditions.

REFERENCE DRAWINGS

Ref. Drawing NO.	DESCRIPTION
—	—

REV	DESCRIPTION	BY	CKD	DATE	APPD	APPD
A	For Review	HASKI	AmerMous	12/01/2024	FELM	SBENZIDIYA
B	For Quotation	AA	LA	22 Mar 2024	FE	SB

APPROVED — ENGINEER — DATE
APPROVED — DISCIPLINE APPROVAL — DATE
APPROVED — PROJECT APPROVAL — DATE

Proj. Approval: S.BENZIDIYA
Discipline Approval: F.ELMOULAOUI
Checked: LAMERMOUSSA
Originator: A.AGOURRAM
Date: 22 Mar 2024
CAD File: Q37092-00-IC-DAL-00005.DWG

PAKMAROC — Pakistan Maroc Phosphore S.A.

JESA

DRAWING
INSTRUMENT LOCATION PLAN

PLAN FROM EL. 521.860 AND ABOVE
PMP CAP PLANT
JORF LASFAR

SCALE	JOB NO.	DRAWING NO.	REV.
1:100	Q37092	Q37092-00-IC-DAL-00005	B